

BASIX
= 277.85 m² of roof area to discharge to water tank.
= stormwater and overflow to discharge to proposed new Kerb Outlet.
o/a= 277.85 m² of roof area.

LEGEND:
● = SURFACE INLETS AS REQUIRED
○ = SURFACE INLETS LINE
--- = STORMWATER LINE


EARTHWORKS TO AHD
HOUSE: FFL RL 16.490 AHD (LIVING)
GARAGE: FFL RL 16.320 AHD
FGL RL 15.995 AHD

NOTE:
REFER TO BASIX CERTIFICATE FOR MORE INFORMATION ON WATER USAGE.


GENERAL DRAINAGE NOTES
1. Roof Plumber to locate Downpipes as indicated on FLOOR PLANS per spec. provided.
2. Stormwater pipes to be 100mm DIA. (Min) at 1 deg. Grade (Min) to AS3500
3. Stormwater pipes may run via sub-floor to achieve minimum Grade to invert level.
4. ALL LEVELS SHOWN ON PLAN ARE APPROXIMATE ONLY UNLESS ACCOMPANIED BY LEVELS PREPARED BY REGISTERED SURVEYOR TO A.H.D
5. Stormwater lines to be Discharged into Existing City Drainage system & connected to local government authority requirements.
NOTE:
EAVES O/H TO ENCROACH AS ALLOWED BY B.C.A:CL3.7.1.7 & FIGURE 3.7.1.9

SYMBOLS & ABBREVIATIONS:		
GP	GULLY PIT	-E- OVERHEAD ELEC LINE
HYD	HYDRANT	-S- SEWER LINE
SIP	SURFACE INLET PIT	GM GAS METER
SIC	SEWER INSPECTION COVER	LP LIGHT POLE
SMH	SEWER MANHOLE	EC ELECTRICITY CONDUIT
WM	WATER METER	ECT ELEC & TELE CONDUIT
EL	ELECTRICITY BOX	TC TELECOM CONDUIT
TP	TELECOM PIT	WC WATER CONDUIT
VC	VEHICLE CROSSING	INV INVERT
SV	STOP VALVE	KO KERB OUTLET
SWMH	STORMWATER MANHOLE	TK TOP OF KERB

LOCALITY SKETCH
UBD AREA: SYD REVISION: 54
MAP: 230 S REF: E15
GPS E

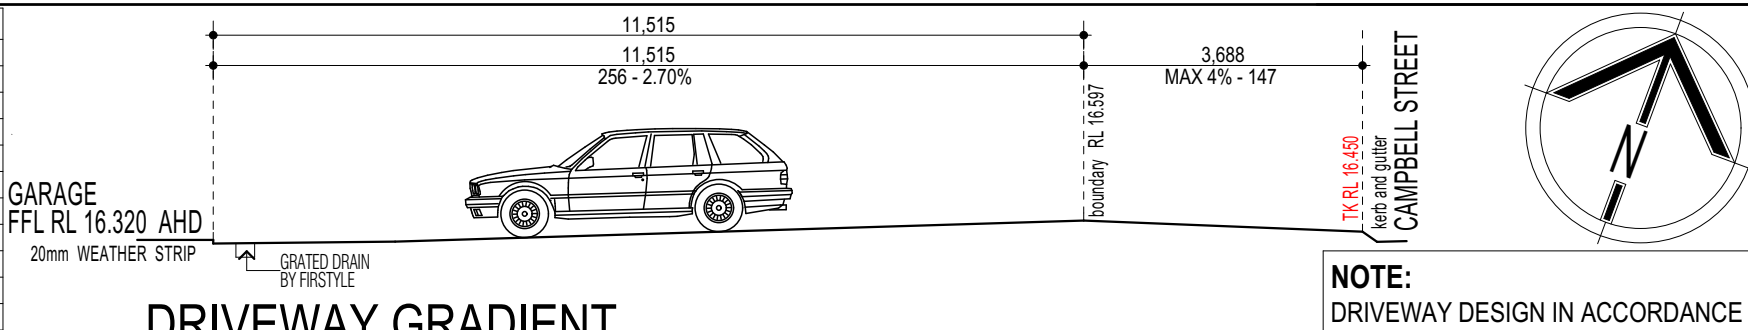

DRIVEWAY GRADIENT
SCALE 1:100
SITE TO BE MICKEY PINNED

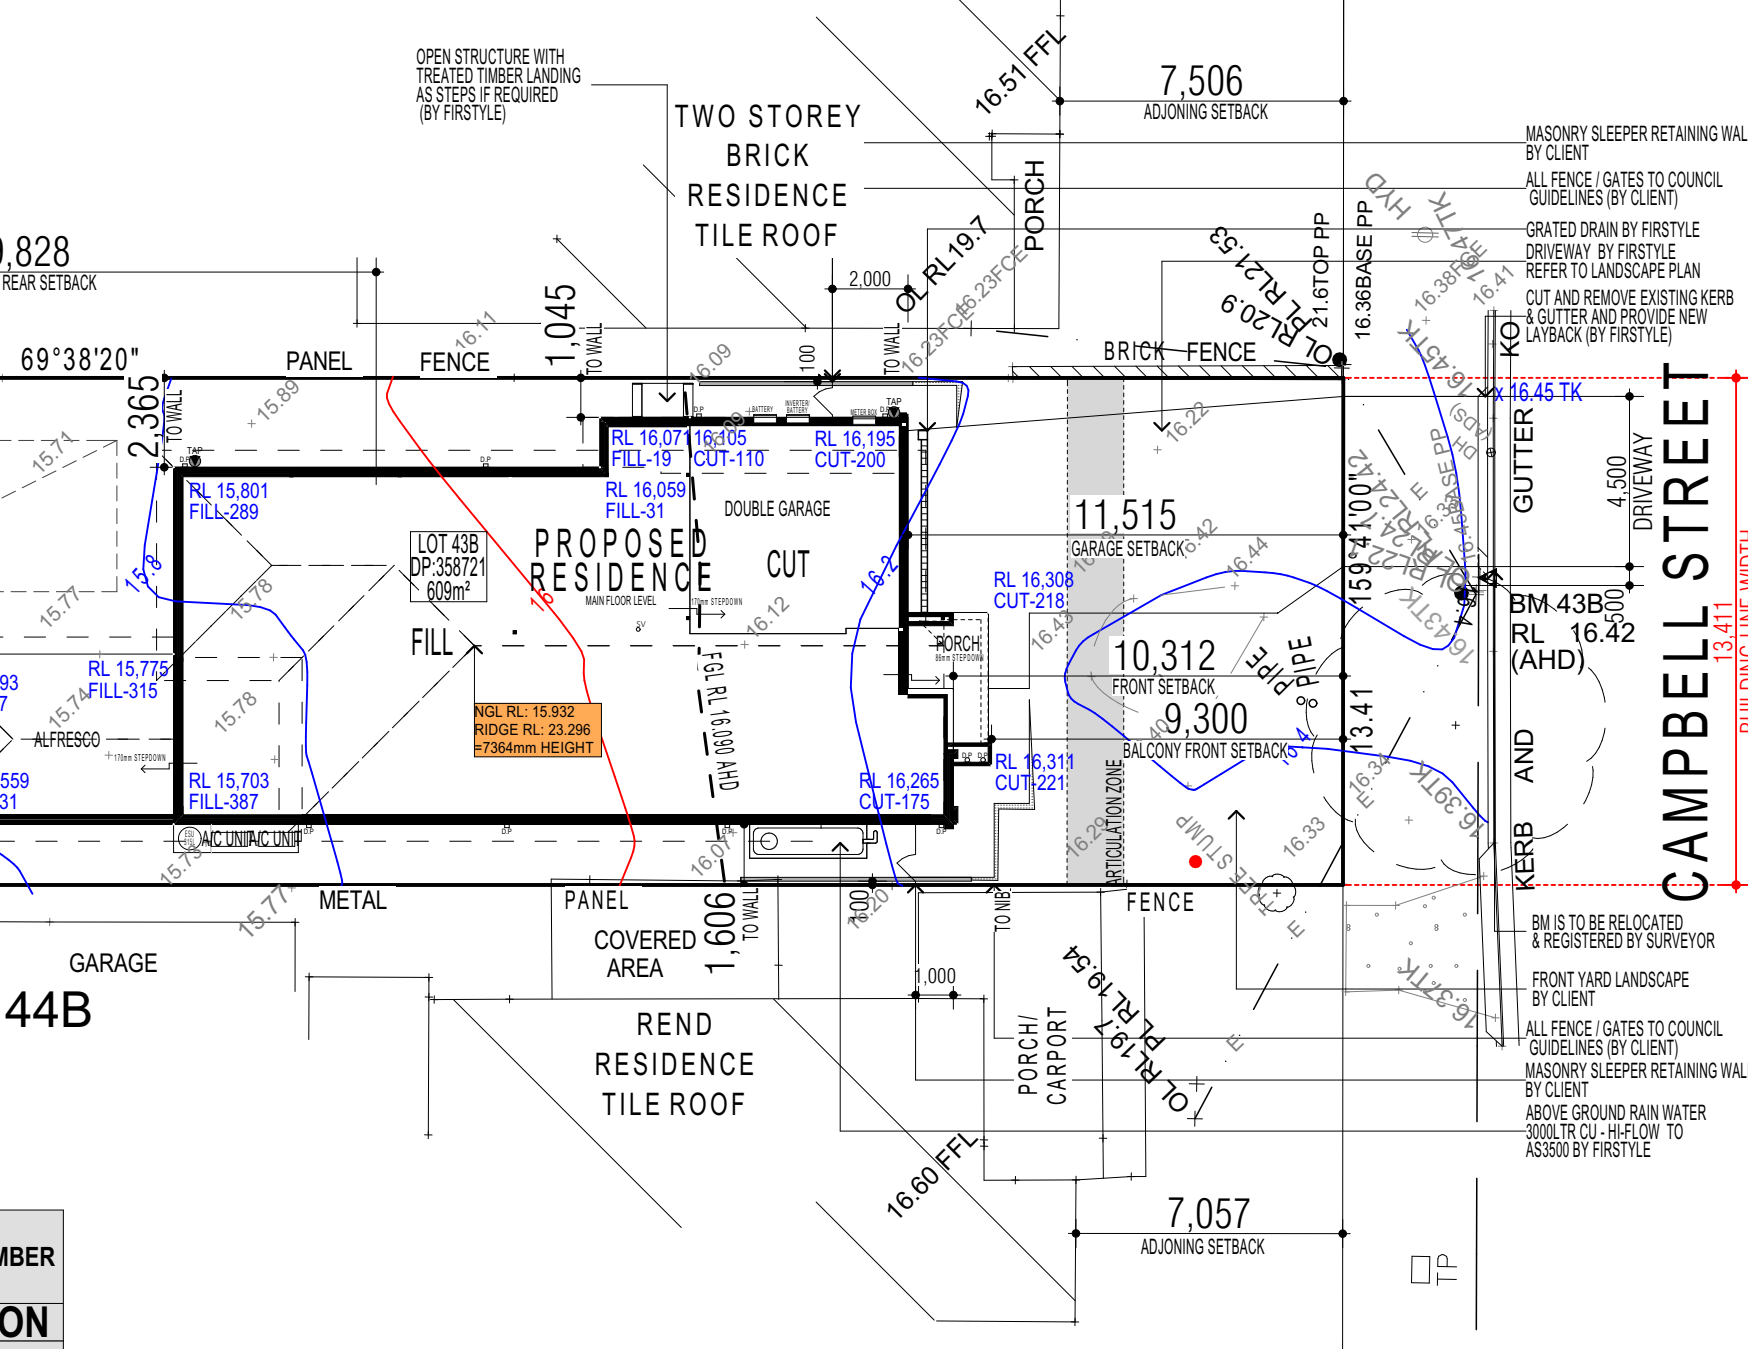

KEY - INDICATIVE ONLY

= JOIST SUPPORT

= NOTE: FLOOR JOISTS TO MANUFACTURERS - SPECIFICATIONS & DETAILS.

= A/C VENTS (APPROX ONLY)


= AIR VENT (APPROX ONLY) LOCATION TO BE NOMINATED ON SITE

= EAVE VENT (APPROX ONLY) TO BE EVENLY SPACED

NOTE:
WATER CONSERVATION DEVICES WITH AAA" RATINGS
· SHOWER HEADS (6 BUT<=7.5L/ MIN)
· WATER TAP OUTLETS
· DUAL FLUSH TOILET SUITES, DUAL FLUSH EQUIVALENT

NOTE:
PROVIDE T2 TERMITE TREATED TIMBER FRAMES
SALINE CONSTRUCTION
NOTE:
PROVIDE FIBRE OPTIC WIRING PACKAGE

NOTE
AIR CONDITIONING ONLY (EER 3.5-4.0 OR GREATER)
SINGLE PHASE POWER TO AS1668 & BCA REQUIREMENTS

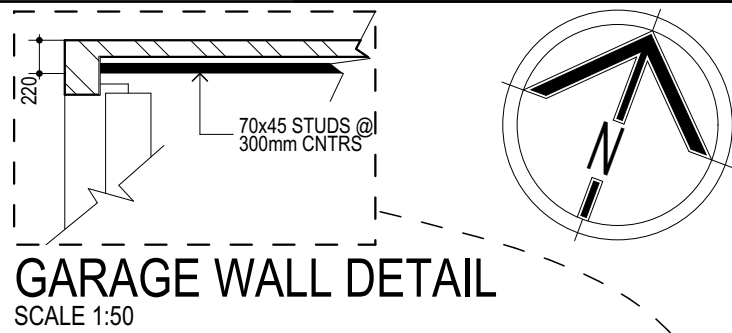

FIRSTSTYLE HOMES

FIRSTSTYLE HOMES Pty Ltd
Lic No. 113412C
ACN. 087 773 779
PO BOX 171, HOXTON PARK 2171


ADMIN: (02) 9731 9600
FAX: (02) 9601 0711
EMAIL: design@firststyle.com.au

HIA members
the best in the business

MASTER BUILDERS ASSOCIATION
MEMBER

MASTER BUILDER, BETTER BUILDER

• ALL WORK TO BE CARRIED OUT IN ACCORDANCE WITH B.C.A. RELEVANT AUSTRALIAN STANDARDS, LOCAL & STATE ORDINANCES, LOCAL ELECTRICITY, WATER REGULATIONS AND ALL OTHER RELEVANT AUTHORITIES CONCERNED.
• ALL ENGINEERING WORK INCLUDING STRUCTURAL, CIVIL AND SITE DRAINAGE TO BE SUBJECT TO ENGINEER'S DETAILS AND CERTIFICATION AS PER REQUIRED BY COUNCIL.
• ALL WORK TO BE CARRIED OUT IN A PROFESSIONAL AND WORKMANSHIP LIKE WORKMANSHIP LIKE MANNER ACCORDING TO THE PLANS AND SPECIFICATION.
• ALL DIMENSIONS ARE TO BE CHECKED & VERIFIED ON SITE BEFORE COMMENCEMENT OF ANY WORK. ALL LEVELS ARE SUBJECT TO FINAL SURVEY AND SETOUT BY REGISTERED SURVEYOR.
• FIRSTSTYLE HOMES SITE SAFETY RULES APPLY.
• DO NOT SCALE FROM DRAWING. LARGER SCALE DRAWINGS & WRITTEN DIMENSIONS TAKE PREFERENCE.
• THIS DRAWING & DESIGN IS COPYRIGHT & THE PROPERTY OF FIRSTSTYLE HOMES, AND MUST NOT BE RETAINED, COPIED OR USED WITHOUT THE AUTHORITY OF THIS FIRM.

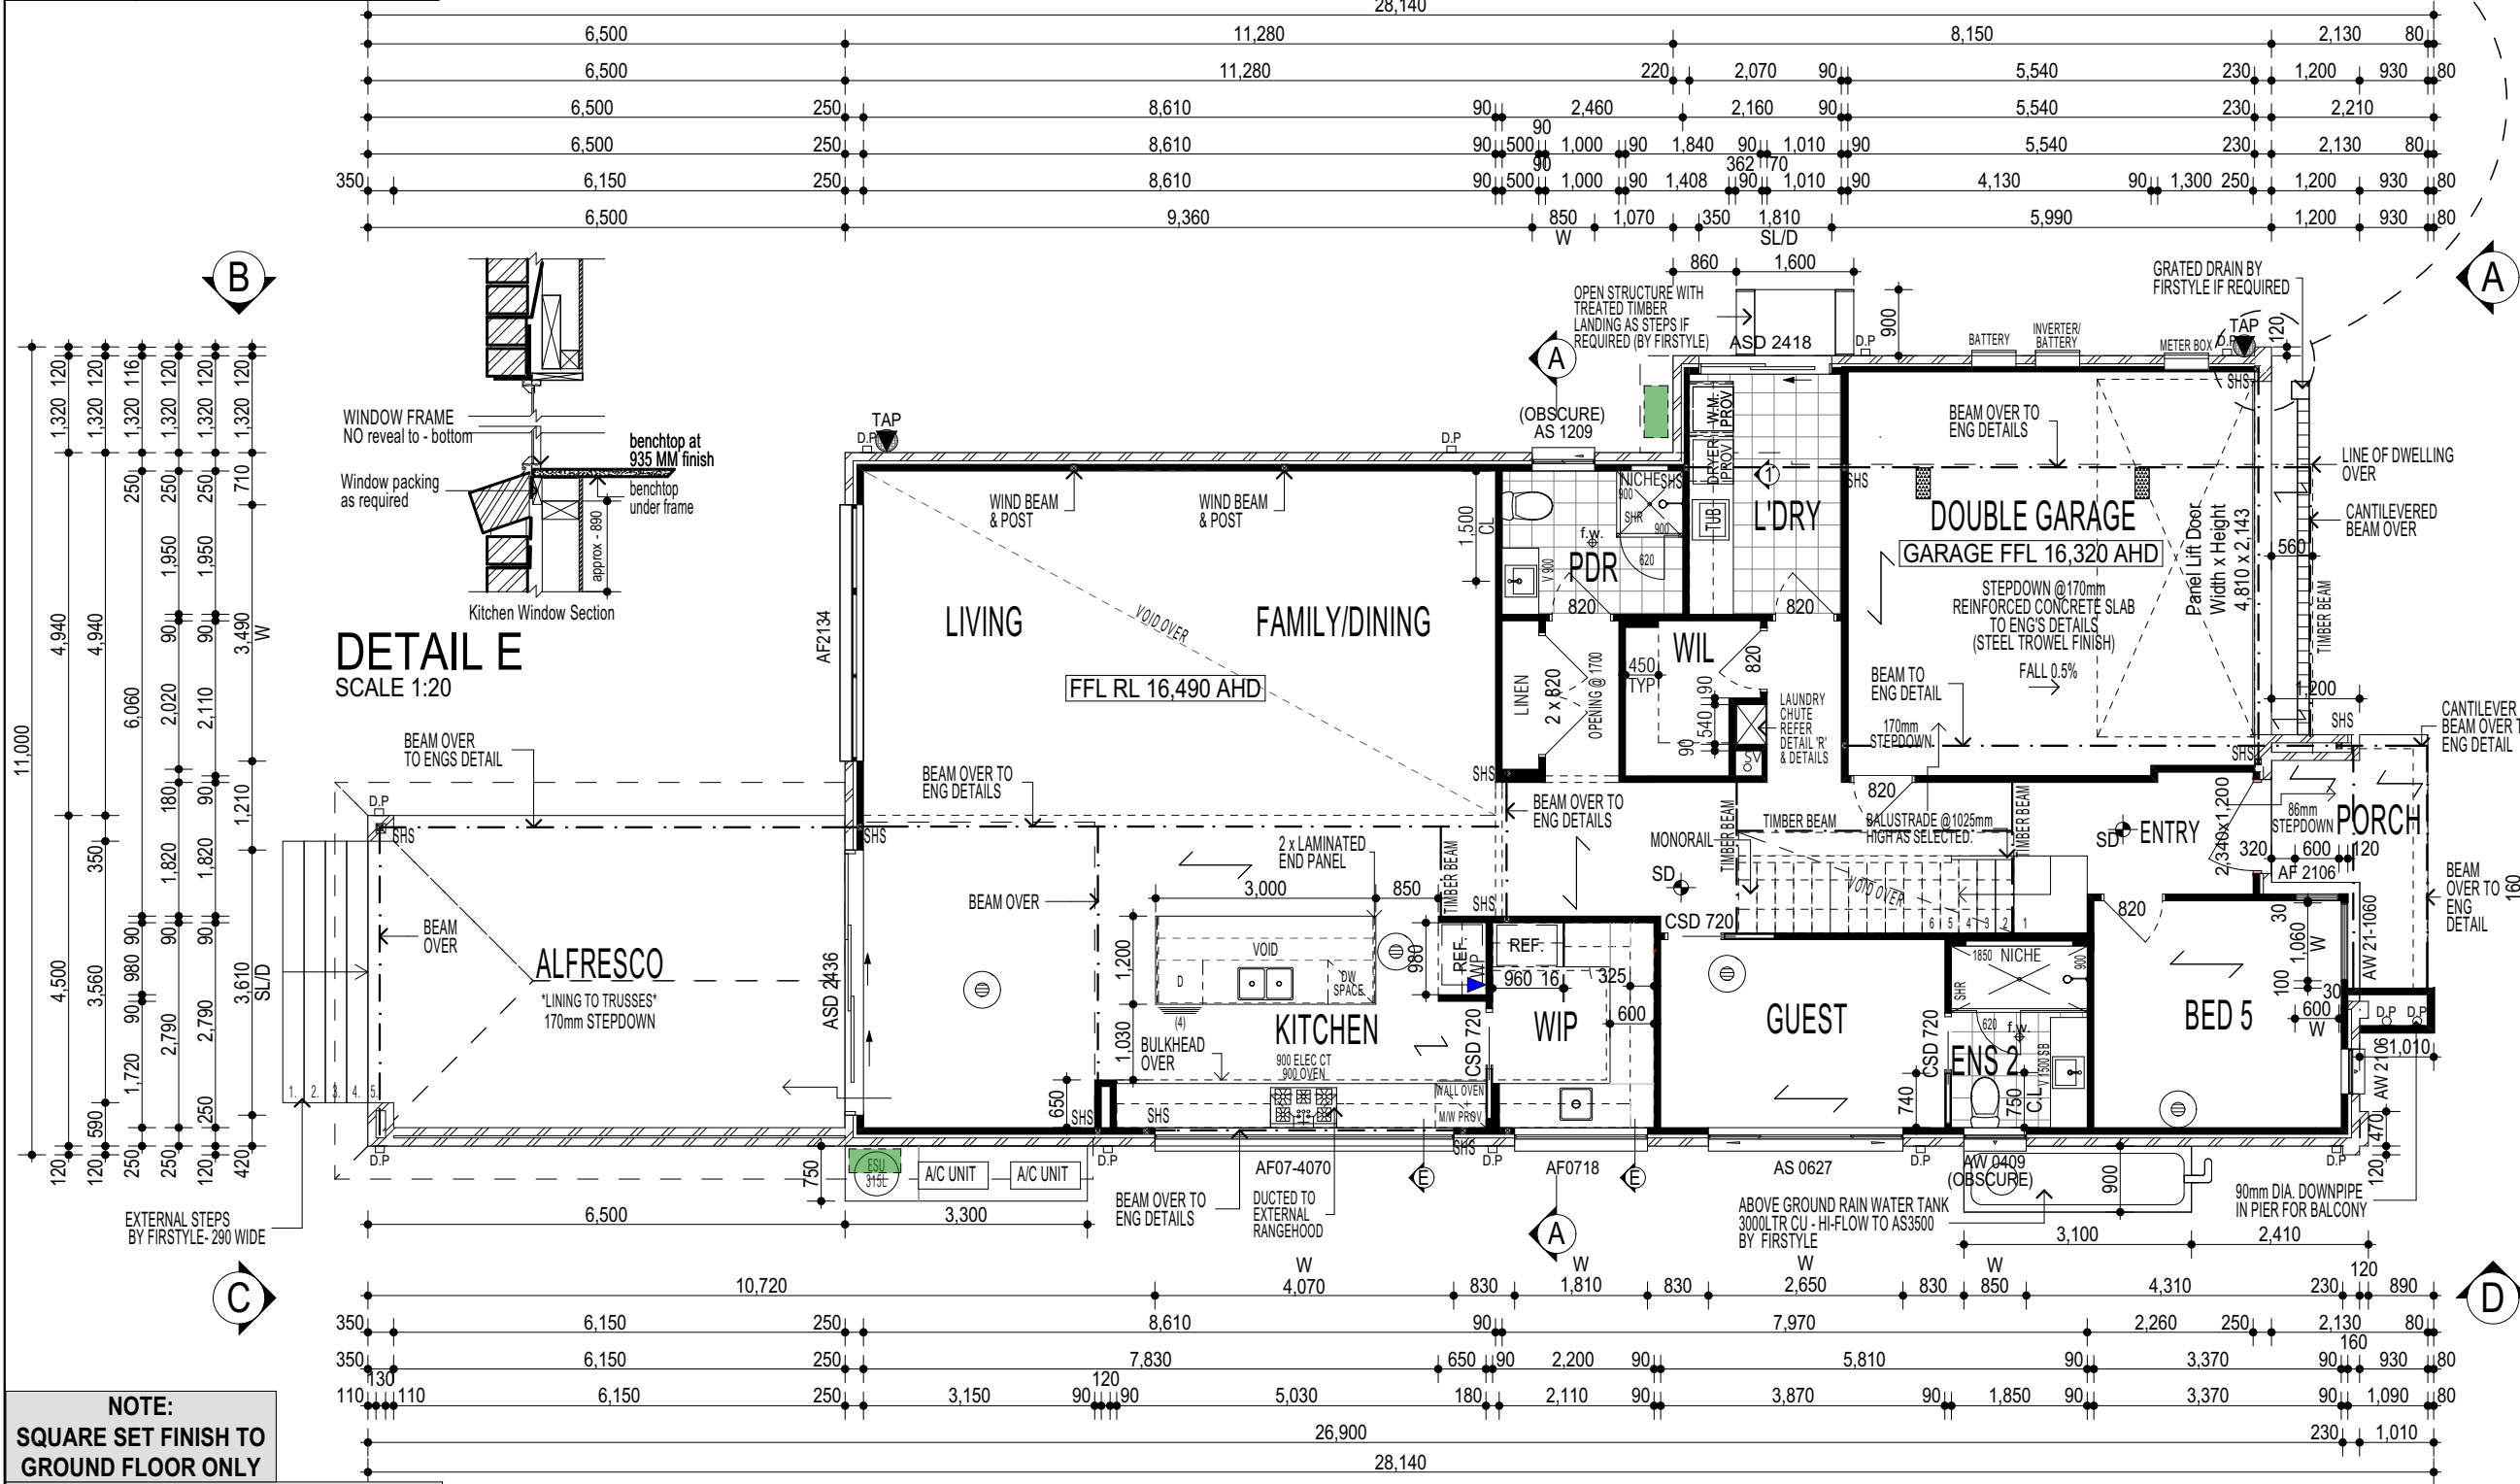

KEY - INDICATIVE ONLY

= JOIST SUPPORT

= NOTE: FLOOR JOISTS TO MANUFACTURES - SPECIFICATIONS & DETAILS.

= A/C VENTS (APPROX ONLY)


= AIR VENT (APPROX ONLY)
LOCATION TO BE NOMINATED ON SITE

= EAVE VENT (APPROX ONLY)
TO BE EVENLY SPACED

NOTE:
WATER CONSERVATION DEVICES WITH AAA" RATINGS
· SHOWER HEADS (6 BUT<=7.5L/ MIN)
· WATER TAP OUTLETS
· DUAL FLUSH TOILET SUITES, DUAL FLUSH EQUIVALENT

NOTE:
PROVIDE T2 TERMITE TREATED TIMBER FRAMES
SALINE CONSTRUCTION
NOTE:
PROVIDE FIBRE OPTIC WIRING PACKAGE

NOTE
AIR CONDITIONING ONLY
(EER 3.5-4.0 OR GREATER)
SINGLE PHASE POWER TO AS1668 & BCA REQUIREMENTS

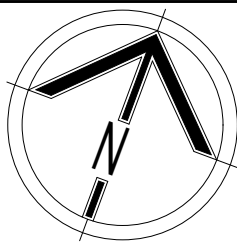

FIRSTSTYLE HOMES

FIRSTSTYLE HOMES Pty.Ltd
Lic No. 113412C
ACN. 087 773 779
PO BOX 171, HOXTON PARK 2171

ADMIN: (02) 9731 9600
FAX : (02) 9601 0711
EMAIL: design@firststyle.com.au

HIA members

the best in the business

MASTER BUILDERS ASSOCIATION

MEMBER

ALL WORK TO BE CARRIED OUT IN ACCORDANCE WITH B.C.A. RELEVANT AUSTRALIAN STANDARDS, LOCAL & STATE ORDINANCES, LOCAL ELECTRICITY, WATER REGULATIONS AND ALL OTHER RELEVANT AUTHORITIES CONCERNED.

ALL ENGINEERING WORK INCLUDING STRUCTURAL, CIVIL AND SITE DRAINAGE TO BE SUBJECT TO ENGINEER'S DETAILS AND CERTIFICATION AS PER REQUIRED BY COUNCIL.

ALL WORK TO BE CARRIED OUT IN A PROFESSIONAL AND WORKMANSHIP LIKE WORKMANSHIP LIKE MANNER ACCORDING TO THE PLANS AND SPECIFICATION.

ALL DIMENSIONS ARE TO BE CHECKED & VERIFIED ON SITE BEFORE COMMENCEMENT OF ANY WORK. ALL LEVELS ARE SUBJECT TO FINAL SURVEY AND SETOUT BY REGISTERED SURVEYOR.

FIRSTSTYLE HOMES SITE SAFETY RULES APPLY.

DO NOT SCALE FROM DRAWING. LARGER SCALE DRAWINGS & WRITTEN DIMENSIONS TAKE PREFERENCE.

THIS DRAWING & DESIGN IS COPYRIGHT & THE PROPERTY OF FIRSTSTYLE HOMES, AND MUST NOT BE RETAINED, COPIED OR USED WITHOUT THE AUTHORITY OF THIS FIRM.



NOTE:
ALL COMPONENTS SUCH AS: APPLIANCES; PLUMBING FITTINGS & FIXTURES; DOORS; CABINETRY; HANDLES; PC ITEMS; ARE SHOWN ON THE PLANS & ELEVATIONS FOR ILLUSTRATION PURPOSES ONLY & TO COMMUNICATE APPROX SIZES. PLEASE REFER TO YOUR SPECIFICATIONS FOR YOUR RELEVANT INCLUSIONS

NOTE:
MUST BE COMPLIANT WITH NEW NATIONAL CONSTRUCTION CODE 2022 AS OF 1st MAY 2023 & CONDENSATION MANAGEMENT PROVISIONS TO COMPLY WITH PART 10.8 OF THE BCA

NOTE:
PROVIDE SHOWER HOBS

NOTE:
FIRST FLOOR WINDOWS TO COMPLY WITH CLAUSE D3D29 OF VOLUME ONE OF THE BCA.

PROMOTION:
LUXE PACK

CLIENT:
H. NGUYEN

LOCATION:
**LOT 43B,
101 CAMPBELL STREET,
FAIRFIELD EAST, NSW , 2165**

DP:
358721

council:
FAIRFIELD

model:
GRANTHAM 36.9 PRISTINE MKII

facade:
9/07/2026

date:
9/07/2026

quotation assessment:
SK1

Sheet:
5 of 12

drawn:
J.U./J.L.P

checked:
P.D.

scale:
1:50


5792-25

CLIENT'S SIGNATURE: _____ DATE: _____ S.P.S.M. _____


FIRST FLOOR PLAN

KEY

- FACE BRICK AS SELECTED
- GRID PANEL SYSTEM CLADDING IN PAINT FINISH (FIRST SELECTION)
- GRID PANEL SYSTEM CLADDING IN PAINT FINISH (SECOND SELECTION)
- RENDER TO BRICKWORK PAINT FINISH (FIRST SELECTION)
- RENDER TO BRICKWORK PAINT FINISH (SECOND SELECTION)
- 150 WIDE VERTICAL CLADDING IN PAINT FINISH AS SELECTED

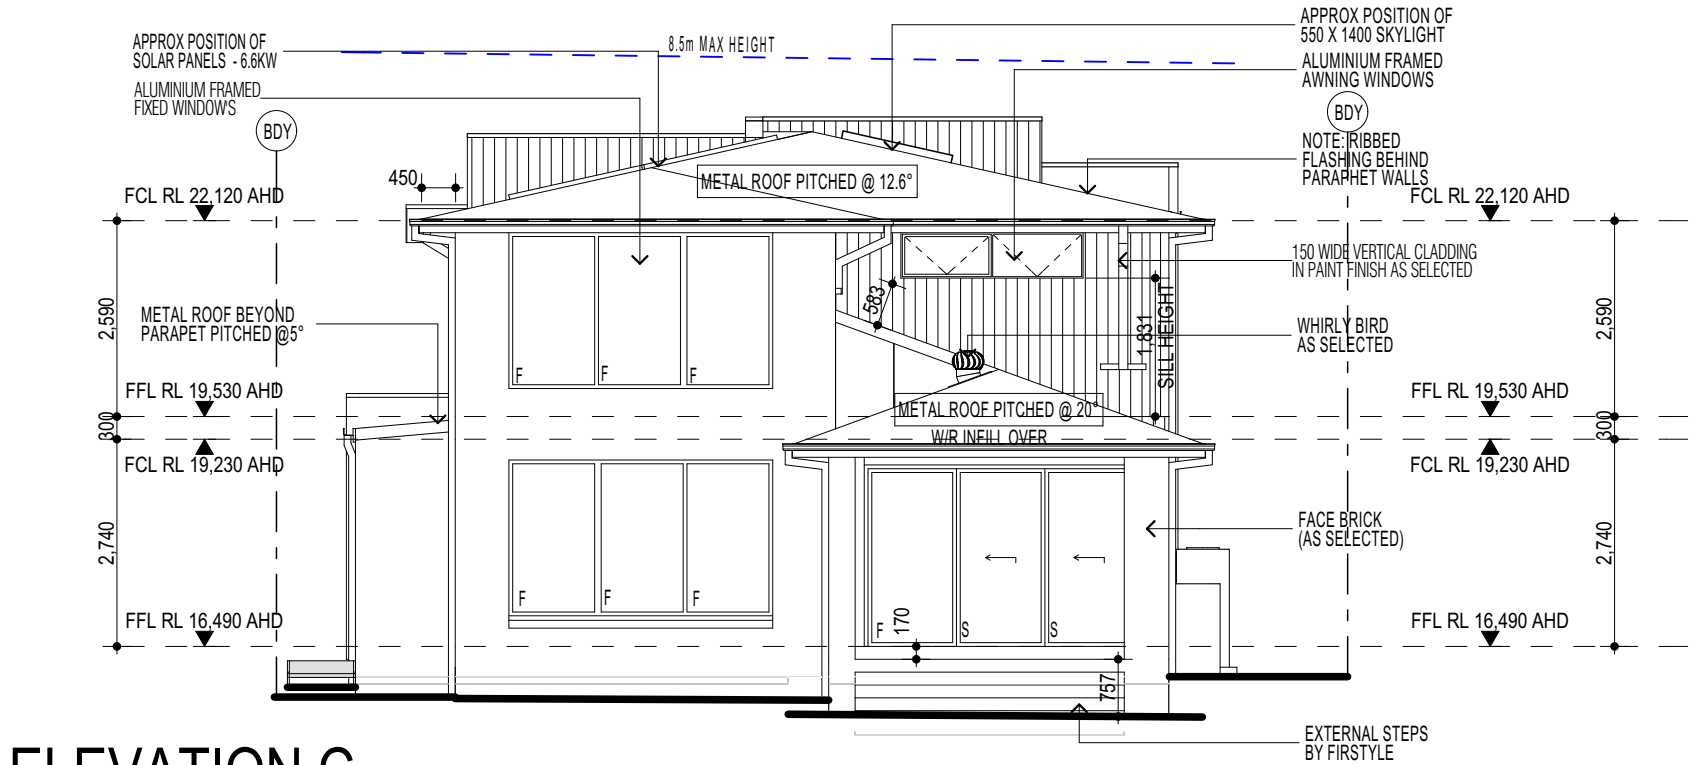

ELEVATION C

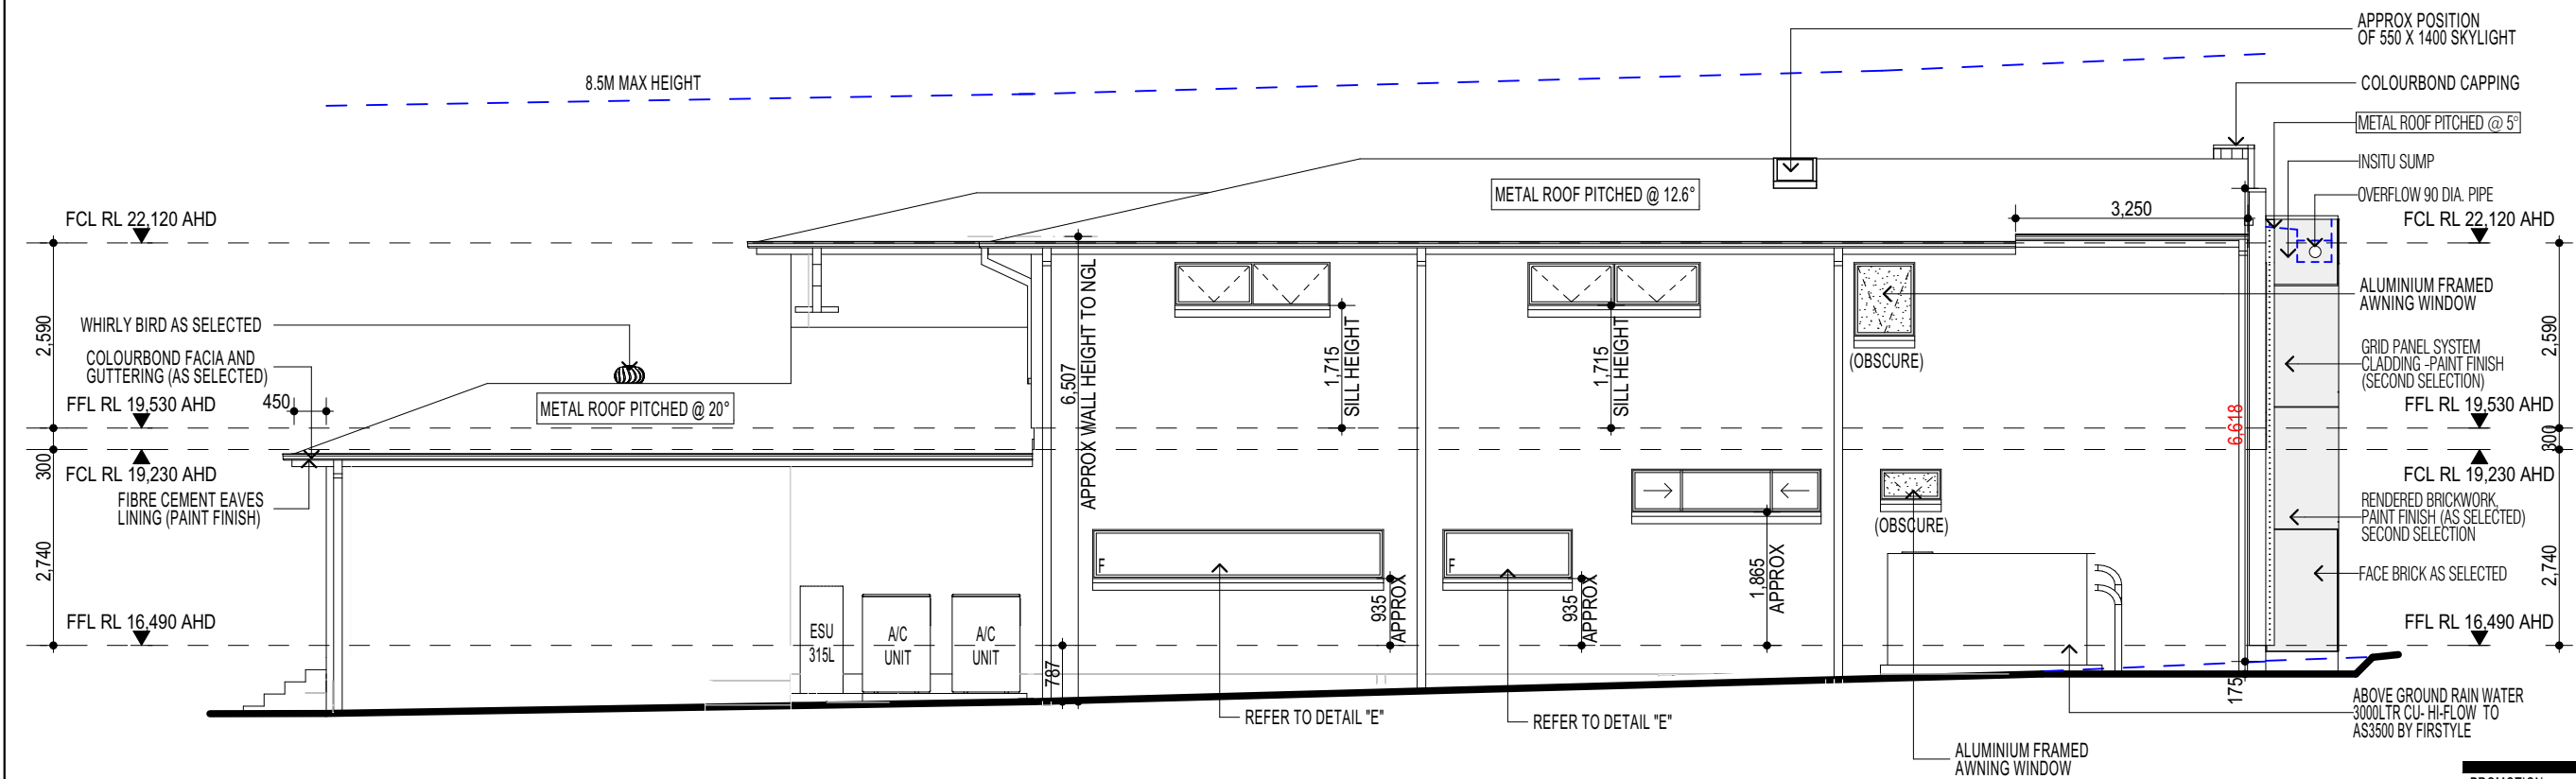

ELEVATION D

NOTE:
ALL COMPONENTS SUCH AS: APPLIANCES; PLUMBING FITTINGS & FIXTURES; DOORS; CABINETRY; HANDLES; PC ITEMS; ARE SHOWN ON THE PLANS & ELEVATIONS FOR ILLUSTRATION PURPOSES ONLY & TO COMMUNICATE APPROX SIZES. PLEASE REFER TO YOUR SPECIFICATIONS FOR YOUR RELEVANT INCLUSIONS

NOTE:
PROVIDE SHOWER HOBS

NOTE:
FIRST FLOOR WINDOWS TO COMPLY WITH CLAUSE D3D29 OF VOLUME ONE OF THE BCA.

NOTE:
PROVIDE T2 TERMITE TREATED TIMBER FRAMES
SALINE CONSTRUCTION
NOTE:
PROVIDE FIBRE OPTIC WIRING PACKAGE

NOTE:
AIR CONDITIONING ONLY (EER 3.5-4.0 OR GREATER)
SINGLE PHASE POWER TO AS1668 & BCA REQUIREMENTS

NOTE:
MUST BE COMPLIANT WITH NEW NATIONAL CONSTRUCTION CODE 2022 AS OF 1st MAY 2023 & CONDENSATION MANAGEMENT PROVISIONS TO COMPLY WITH PART 10.8 OF THE BCA

FIRSTYLE HOMES

FIRSTYLE HOMES Pty.Ltd
Lic No. 113412C
ACN. 087 773 779
PO BOX 171, HOXTON PARK 2171

ADMIN: (02) 9731 9600
FAX: (02) 9601 0711
EMAIL: design@firststyle.com.au

HIA members
the best in the business

MASTER BUILDERS ASSOCIATION
MEMBER
MASTER BUILDER, BETTER BUILDER


- ALL WORK TO BE CARRIED OUT IN ACCORDANCE WITH B.C.A. RELEVANT AUSTRALIAN STANDARDS, LOCAL & STATE ORDINANCES, LOCAL ELECTRICITY, WATER REGULATIONS AND ALL OTHER RELEVANT AUTHORITIES CONCERNED.
- ALL ENGINEERING WORK INCLUDING STRUCTURAL, CIVIL AND SITE DRAINAGE TO BE SUBJECT TO ENGINEER'S DETAILS AND CERTIFICATION AS PER REQUIRED BY COUNCIL.
- ALL WORK TO BE CARRIED OUT IN A PROFESSIONAL AND WORKMANSHIP LIKE WORKMANSHIP LIKE MANNER ACCORDING TO THE PLANS AND SPECIFICATION.
- ALL DIMENSIONS ARE TO BE CHECKED & VERIFIED ON SITE BEFORE COMMENCEMENT OF ANY WORK. ALL LEVELS ARE SUBJECT TO FINAL SURVEY AND SETOUT BY REGISTERED SURVEYOR.
- FIRSTYLE HOMES SITE SAFETY RULES APPLY.
- DO NOT SCALE FROM DRAWING. LARGER SCALE DRAWINGS & WRITTEN DIMENSIONS TAKE PREFERENCE.
- THIS DRAWING & DESIGN IS COPYRIGHT & THE PROPERTY OF FIRSTYLE HOMES, AND MUST NOT BE RETAINED, COPIED OR USED WITHOUT THE AUTHORITY OF THIS FIRM.

ELEVATIONS


PROMOTION: LUXE PACK			
CLIENT: H. NGUYEN			
LOCATION: LOT 43B, 101 CAMPBELL STREET, FAIRFIELD EAST, NSW , 2165			
DP: 358721	model: GRANTHAM 36.9 PRISTINE MKII	facade: J.U./J.L.P	council: FAIRFIELD
date: 9/07/2026	checked: P.D.	scale: 1:100	quotation assessment: SK1
Sheet: 7 of 12	drawn: J.U./J.L.P	checked: P.D.	5792-25
CLIENTS SIGNATURE:		DATE:	
		S.P.S.M...	

KEY

- FACE BRICK AS SELECTED
- GRID PANEL SYSTEM CLADDING IN PAINT FINISH (FIRST SELECTION)
- GRID PANEL SYSTEM CLADDING IN PAINT FINISH (SECOND SELECTION)
- RENDER TO BRICKWORK PAINT FINISH (FIRST SELECTION)
- RENDER TO BRICKWORK PAINT FINISH (SECOND SELECTION)
- 150 WIDE VERTICAL CLADDING IN PAINT FINISH AS SELECTED

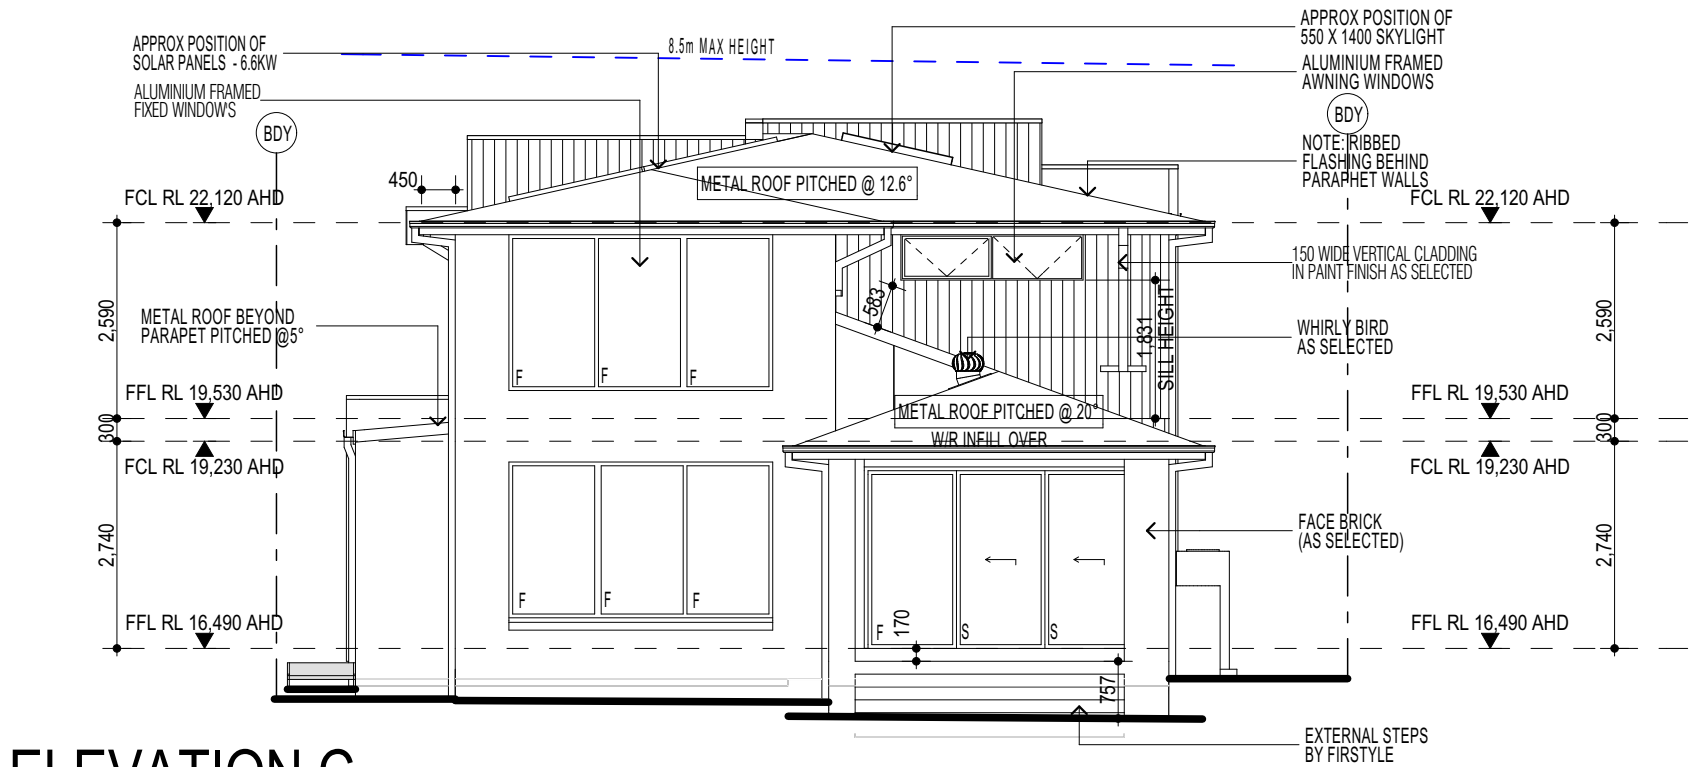

ELEVATION C

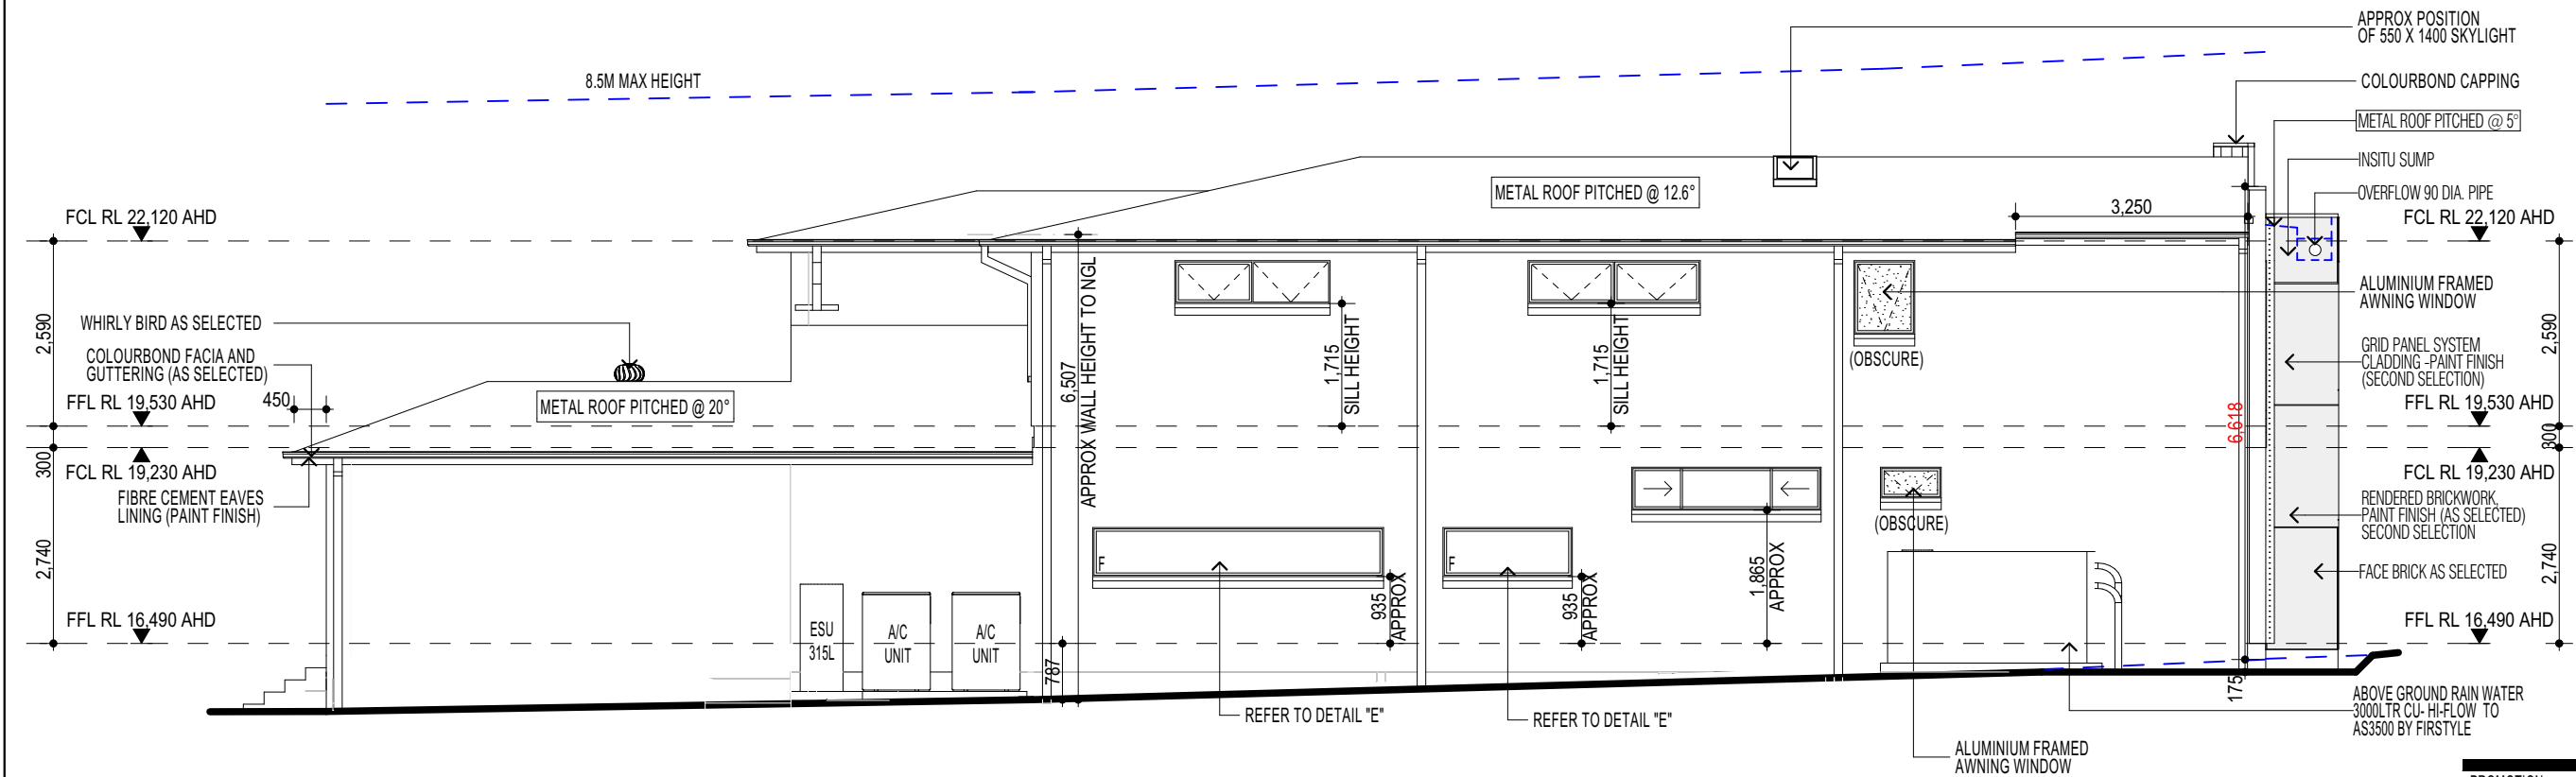

ELEVATION D

NOTE:
ALL COMPONENTS SUCH AS: APPLIANCES; PLUMBING FITTINGS & FIXTURES; DOORS; CABINETRY; HANDLES; PC ITEMS; ARE SHOWN ON THE PLANS & ELEVATIONS FOR ILLUSTRATION PURPOSES ONLY & TO COMMUNICATE APPROX SIZES. PLEASE REFER TO YOUR SPECIFICATIONS FOR YOUR RELEVANT INCLUSIONS

NOTE:
PROVIDE SHOWER HOBS

NOTE:
FIRST FLOOR WINDOWS TO COMPLY WITH CLAUSE D3D29 OF VOLUME ONE OF THE BCA.

NOTE:
PROVIDE T2 TERMITE TREATED TIMBER FRAMES

SALINE CONSTRUCTION

NOTE:
PROVIDE FIBRE OPTIC WIRING PACKAGE

NOTE:
AIR CONDITIONING ONLY (EER 3.5-4.0 OR GREATER) SINGLE PHASE POWER TO AS1668 & BCA REQUIREMENTS

NOTE:
MUST BE COMPLIANT WITH NEW NATIONAL CONSTRUCTION CODE 2022 AS OF 1st MAY 2023 & CONDENSATION MANAGEMENT PROVISIONS TO COMPLY WITH PART 10.8 OF THE BCA

FIRSTSTYLE HOMES

FIRSTSTYLE HOMES Pty.Ltd
Lic No. 113412C
ACN. 087 773 779
PO BOX 171, HOXTON PARK 2171

ADMIN: (02) 9731 9600
FAX: (02) 9601 0711
EMAIL: design@firststyle.com.au

HIA members
the best in the business

MASTER BUILDERS ASSOCIATION
MEMBER
MASTER BUILDER, BETTER BUILDER

- ALL WORK TO BE CARRIED OUT IN ACCORDANCE WITH B.C.A. RELEVANT AUSTRALIAN STANDARDS, LOCAL & STATE ORDINANCES, LOCAL ELECTRICITY, WATER REGULATIONS AND ALL OTHER RELEVANT AUTHORITIES CONCERNED.
- ALL ENGINEERING WORK INCLUDING STRUCTURAL, CIVIL AND SITE DRAINAGE TO BE SUBJECT TO ENGINEER'S DETAILS AND CERTIFICATION AS PER REQUIRED BY COUNCIL.
- ALL WORK TO BE CARRIED OUT IN A PROFESSIONAL AND WORKMANSHIP LIKE WORKMANSHIP LIKE MANNER ACCORDING TO THE PLANS AND SPECIFICATION.
- ALL DIMENSIONS ARE TO BE CHECKED & VERIFIED ON SITE BEFORE COMMENCEMENT OF ANY WORK. ALL LEVELS ARE SUBJECT TO FINAL SURVEY AND SETOUT BY REGISTERED SURVEYOR.
- FIRSTSTYLE HOMES SITE SAFETY RULES APPLY.
- DO NOT SCALE FROM DRAWING. LARGER SCALE DRAWINGS & WRITTEN DIMENSIONS TAKE PREFERENCE.
- THIS DRAWING & DESIGN IS COPYRIGHT & THE PROPERTY OF FIRSTSTYLE HOMES, AND MUST NOT BE RETAINED, COPIED OR USED WITHOUT THE AUTHORITY OF THIS FIRM.

ELEVATIONS

PROMOTION:
LUXE PACK

CLIENT:
H. NGUYEN

LOCATION:
**LOT 43B,
101 CAMPBELL STREET,
FAIRFIELD EAST, NSW , 2165**

DP:
358721

model:
GRANTHAM 36.9 PRISTINE MKII

Sheet:
7 of 12

council:
FAIRFIELD

date:
9/07/2026

quotation assessment:
SK1

checked:
J.U./J.L.P.

P.D.


scale: 1:100

5792-25

CLIENTS SIGNATURE: _____ DATE: _____ S.P.S.M. _____


KEY

- FACE BRICK AS SELECTED
- GRID PANEL SYSTEM CLADDING IN PAINT FINISH (FIRST SELECTION)
- GRID PANEL SYSTEM CLADDING IN PAINT FINISH (SECOND SELECTION)
- RENDER TO BRICKWORK PAINT FINISH (FIRST SELECTION)
- RENDER TO BRICKWORK PAINT FINISH (SECOND SELECTION)
- 150 WIDE VERTICAL CLADDING IN PAINT FINISH AS SELECTED

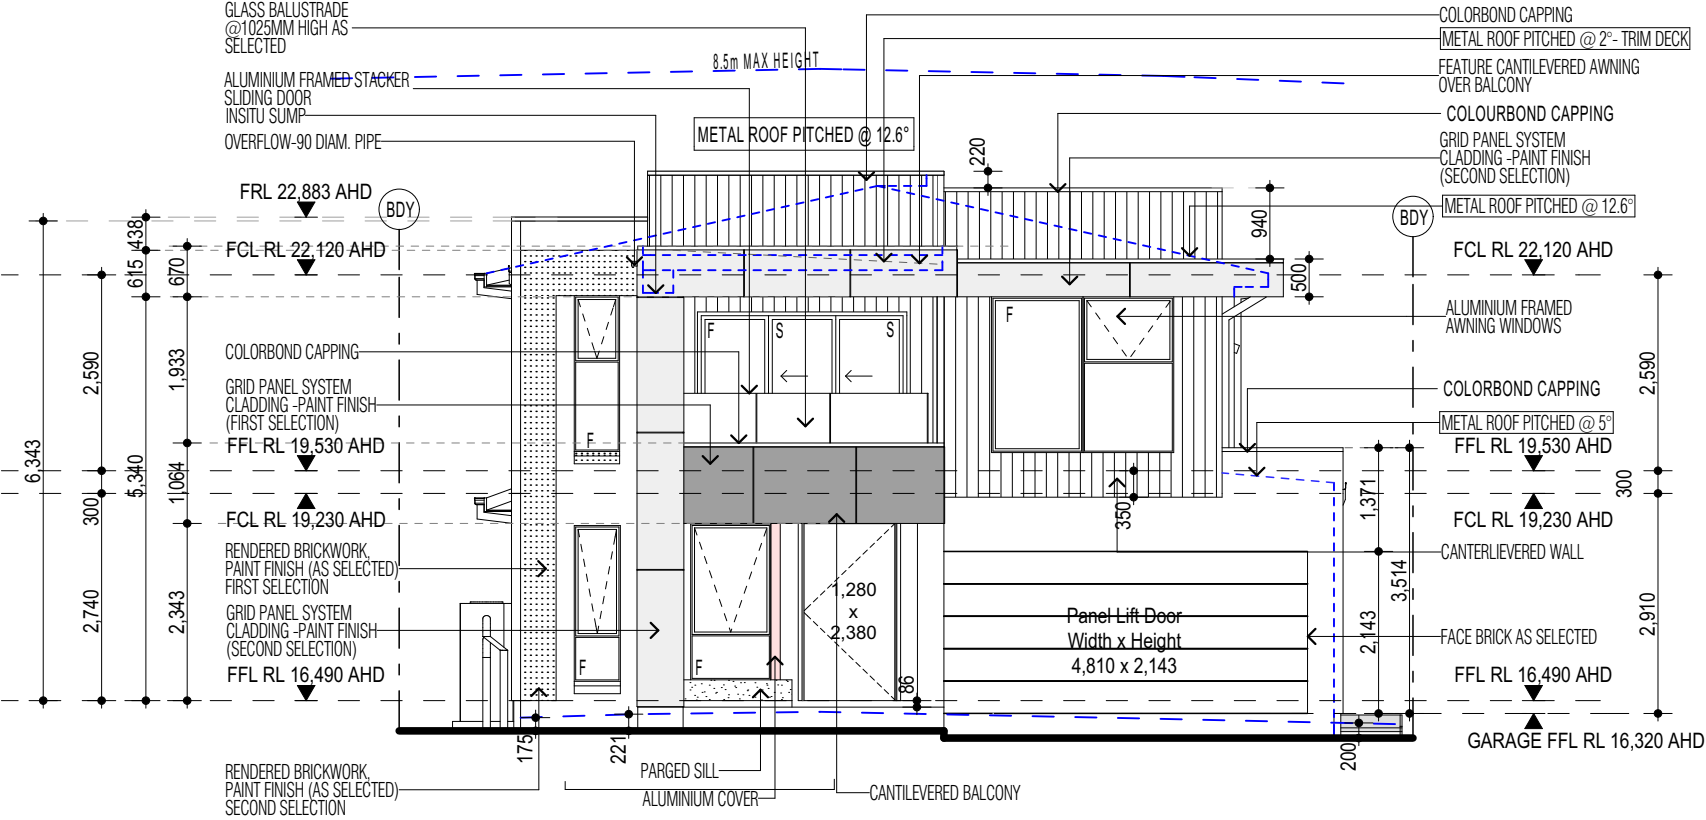

ELEVATION A

8.5M MAX HEIGHT

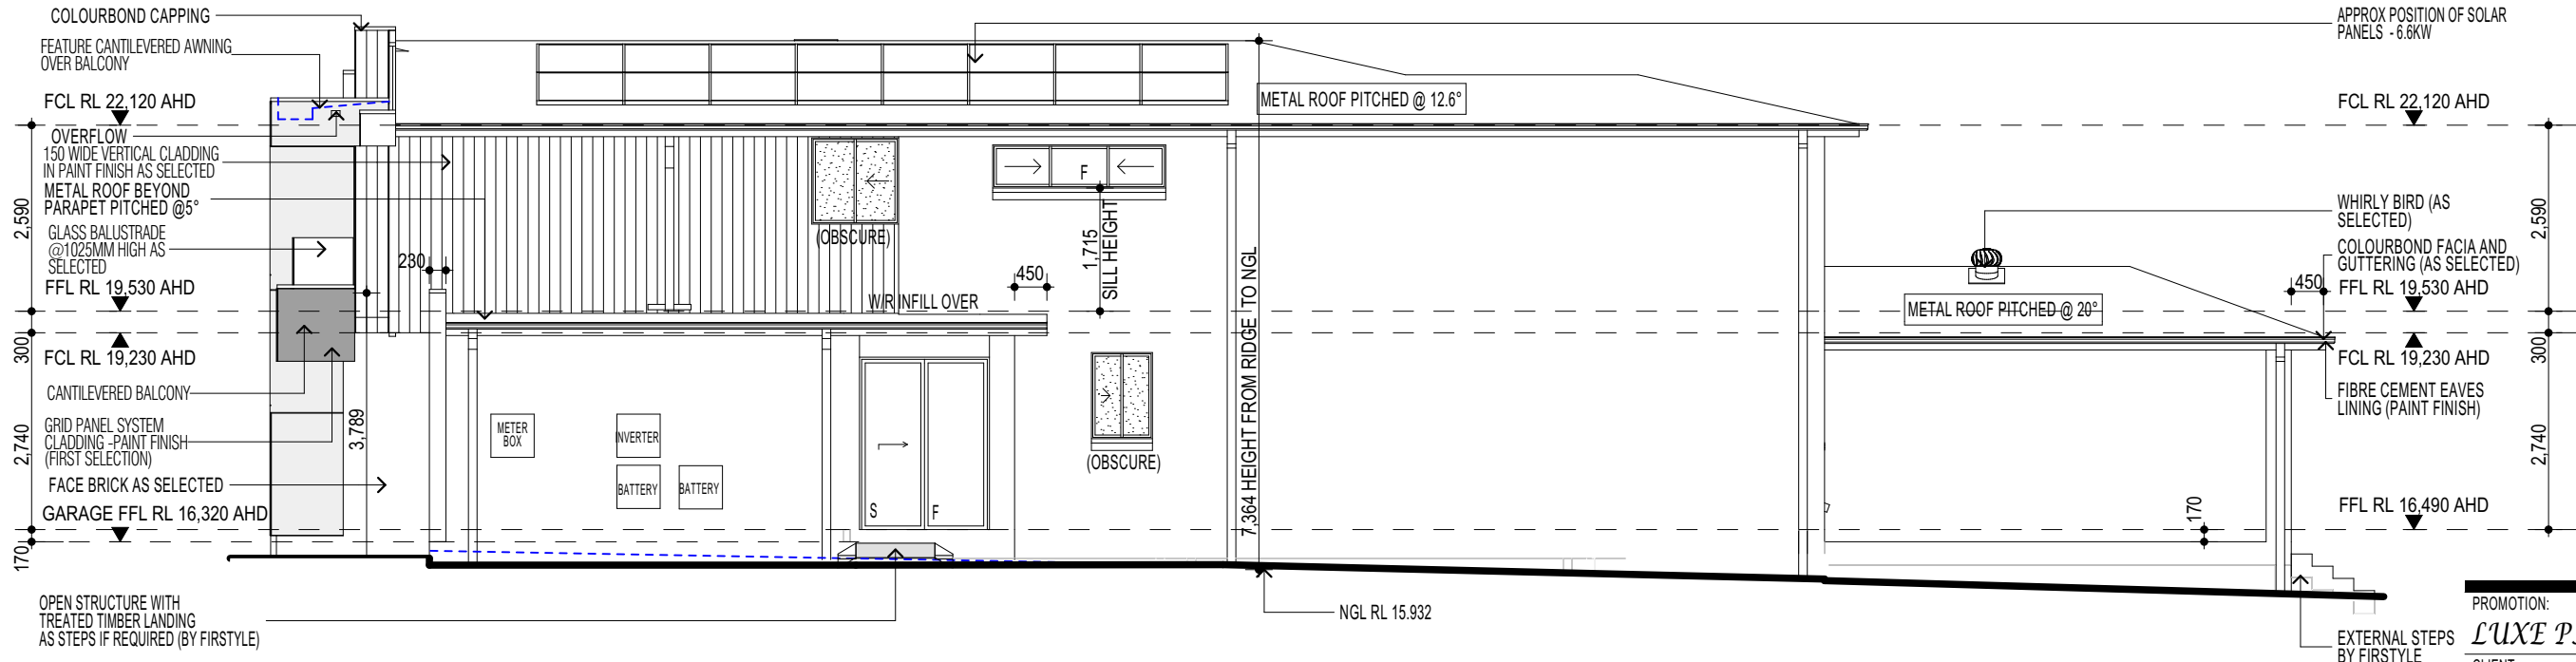

ELEVATION B

NOTE:
ALL COMPONENTS SUCH AS: APPLIANCES; PLUMBING FITTINGS & FIXTURES; DOORS; CABINETS; HANDLES; PC ITEMS; ARE SHOWN ON THE PLANS & ELEVATIONS FOR ILLUSTRATION PURPOSES ONLY & TO COMMUNICATE APPROX SIZES. PLEASE REFER TO YOUR SPECIFICATIONS FOR YOUR RELEVANT INCLUSIONS

NOTE:
PROVIDE SHOWER HOBS

NOTE:
PROVIDE T2 TERMITE TREATED TIMBER FRAMES

NOTE:
FIRST FLOOR WINDOWS TO COMPLY WITH CLAUSE D3D29 OF VOLUME ONE OF THE BCA.

SALINE CONSTRUCTION

NOTE:
PROVIDE FIBRE OPTIC WIRING PACKAGE

NOTE:
AIR CONDITIONING ONLY (EER 3.5-4.0 OR GREATER) SINGLE PHASE POWER TO AS1668 & BCA REQUIREMENTS

NOTE:
MUST BE COMPLIANT WITH NEW NATIONAL CONSTRUCTION CODE 2022 AS OF 1st MAY 2023 & CONDENSATION MANAGEMENT PROVISIONS TO COMPLY WITH PART 10.8 OF THE BCA

FIRSTSTYLE HOMES

FIRSTSTYLE HOMES Pty Ltd
Lic No. 113412C
ACN: 087 773 779
PO BOX 171, HOXTON PARK 2171

ADMIN: (02) 9731 9600
FAX: (02) 9601 0711
EMAIL: design@firststyle.com.au

HIA members
the best in the business

MASTER BUILDERS ASSOCIATION
MEMBER

• ALL WORK TO BE CARRIED OUT IN ACCORDANCE WITH B.C.A. RELEVANT AUSTRALIAN STANDARDS, LOCAL & STATE ORDINANCES, LOCAL ELECTRICITY, WATER REGULATIONS AND ALL OTHER RELEVANT AUTHORITIES CONCERNED.
• ALL ENGINEERING WORK INCLUDING STRUCTURAL, CIVIL AND SITE DRAINAGE TO BE SUBJECT TO ENGINEER'S DETAILS AND CERTIFICATION AS PER REQUIRED BY COUNCIL.
• ALL WORK TO BE CARRIED OUT IN A PROFESSIONAL AND WORKMANSHIP LIKE WORKMANSHIP LIKE MANNER ACCORDING TO THE PLANS AND SPECIFICATION.
• ALL DIMENSIONS ARE TO BE CHECKED & VERIFIED ON SITE BEFORE COMMENCEMENT OF ANY WORK. ALL LEVELS ARE SUBJECT TO FINAL SURVEY AND SETOUT BY REGISTERED SURVEYOR.
• FIRSTSTYLE HOMES SITE SAFETY RULES APPLY.
• DO NOT SCALE FROM DRAWING. LARGER SCALE DRAWINGS & WRITTEN DIMENSIONS TAKE PREFERENCE.
• THIS DRAWING & DESIGN IS COPYRIGHT & THE PROPERTY OF FIRSTSTYLE HOMES, AND MUST NOT BE RETAINED, COPIED OR USED WITHOUT THE AUTHORITY OF THIS FIRM.

PROMOTION: **LUXE PACK**

CLIENT: **H. NGUYEN**

LOCATION: **LOT 43B, 101 CAMPBELL STREET, FAIRFIELD EAST, NSW, 2165**

DP: 358721
model: GRANTHAM 36.9 PRISTINE MKII
Sheet: 6 of 12

council: FAIRFIELD
date: 9/07/2026
checked: J.U./J.L.P.
scale: 1:100

quotation assessment: SK1
5792-25

CLIENT'S SIGNATURE: _____ DATE: _____ S.P.S.M.:

ELEVATIONS

- NOTE**
- ELECTRIC OVEN SHOWN ONLY, NO ALLOWANCE HAS BEEN MADE FOR GAS OVEN.
 - SIZES OF FIXTURES MAY VARY DEPENDING ON PRODUCT SELECTION.
 - HEIGHT OF TILES MAY VARY ACCORDING TO SELECTION OF TILES.
 - ALL DIMENSIONS AND LAYOUTS OF ALL CUPBOARDS SHOWN ARE NOMINAL ONLY AND ARE SUBJECT TO MANUFACTURERS DETAILED DRAWINGS & ON SITE MEASURE
 - REFRIGERATOR'S HEIGHT TO BE 1840mm AND 930mm FINISH WIDTH OPENING UNLESS NOTED OTHERWISE ON PLANS AND SPECIFICATIONS.
 - BENCH TOP FINISH HEIGHT 935mm

DISHWASHER PROVISION (if applicable)
SIZE _____

MICROWAVE PROVISION (if applicable)
SIZE _____

REFRIGERATOR OPENING SIZE _____

COOKTOP MODEL _____

OVEN MODEL _____

RANGEHOOD MODEL _____

SINK MODEL _____


BENCHTOP COLOUR _____

DOOR COLOUR _____

KICKBOARD COLOUR _____

HARDWARE TYPE _____

PANTRY DOOR/S _____

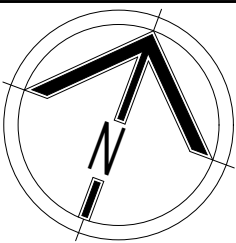



FIRSTSTYLE HOMES

FIRSTSTYLE HOMES Pty.Ltd
Lic No. 113412C
ACN. 087 773 779
PO BOX 171, HOXTON PARK 2171

ADMIN: (02) 9731 9600
FAX: (02) 9601 0711
EMAIL: design@firststyle.com.au


HIA members
the best in the business





MASTER BUILDERS ASSOCIATION
MEMBER
MASTER BUILDER, BETTER BUILDER

- ALL WORK TO BE CARRIED OUT IN ACCORDANCE WITH B.C.A. RELEVANT AUSTRALIAN STANDARDS, LOCAL & STATE ORDINANCES, LOCAL ELECTRICITY, WATER REGULATIONS AND ALL OTHER RELEVANT AUTHORITIES CONCERNED.
- ALL ENGINEERING WORK INCLUDING STRUCTURAL, CIVIL AND SITE DRAINAGE TO BE SUBJECT TO ENGINEER'S DETAILS AND CERTIFICATION AS PER REQUIRED BY COUNCIL.
- ALL WORK TO BE CARRIED OUT IN A PROFESSIONAL AND WORKMANSHIP LIKE WORKMANSHIP LIKE MANNER ACCORDING TO THE PLANS AND SPECIFICATION.
- ALL DIMENSIONS ARE TO BE CHECKED & VERIFIED ON SITE BEFORE COMMENCEMENT OF ANY WORK, ALL LEVELS ARE SUBJECT TO FINAL SURVEY AND SETOUT BY REGISTERED SURVEYOR.
- FIRSTSTYLE HOMES SITE SAFETY RULES APPLY.
- DO NOT SCALE FROM DRAWING. LARGER SCALE DRAWINGS & WRITTEN DIMENSIONS TAKE PREFERENCE.
- THIS DRAWING & DESIGN IS COPYRIGHT & THE PROPERTY OF FIRSTSTYLE HOMES, AND MUST NOT BE RETAINED, COPIED OR USED WITHOUT THE AUTHORITY OF THIS FIRM.

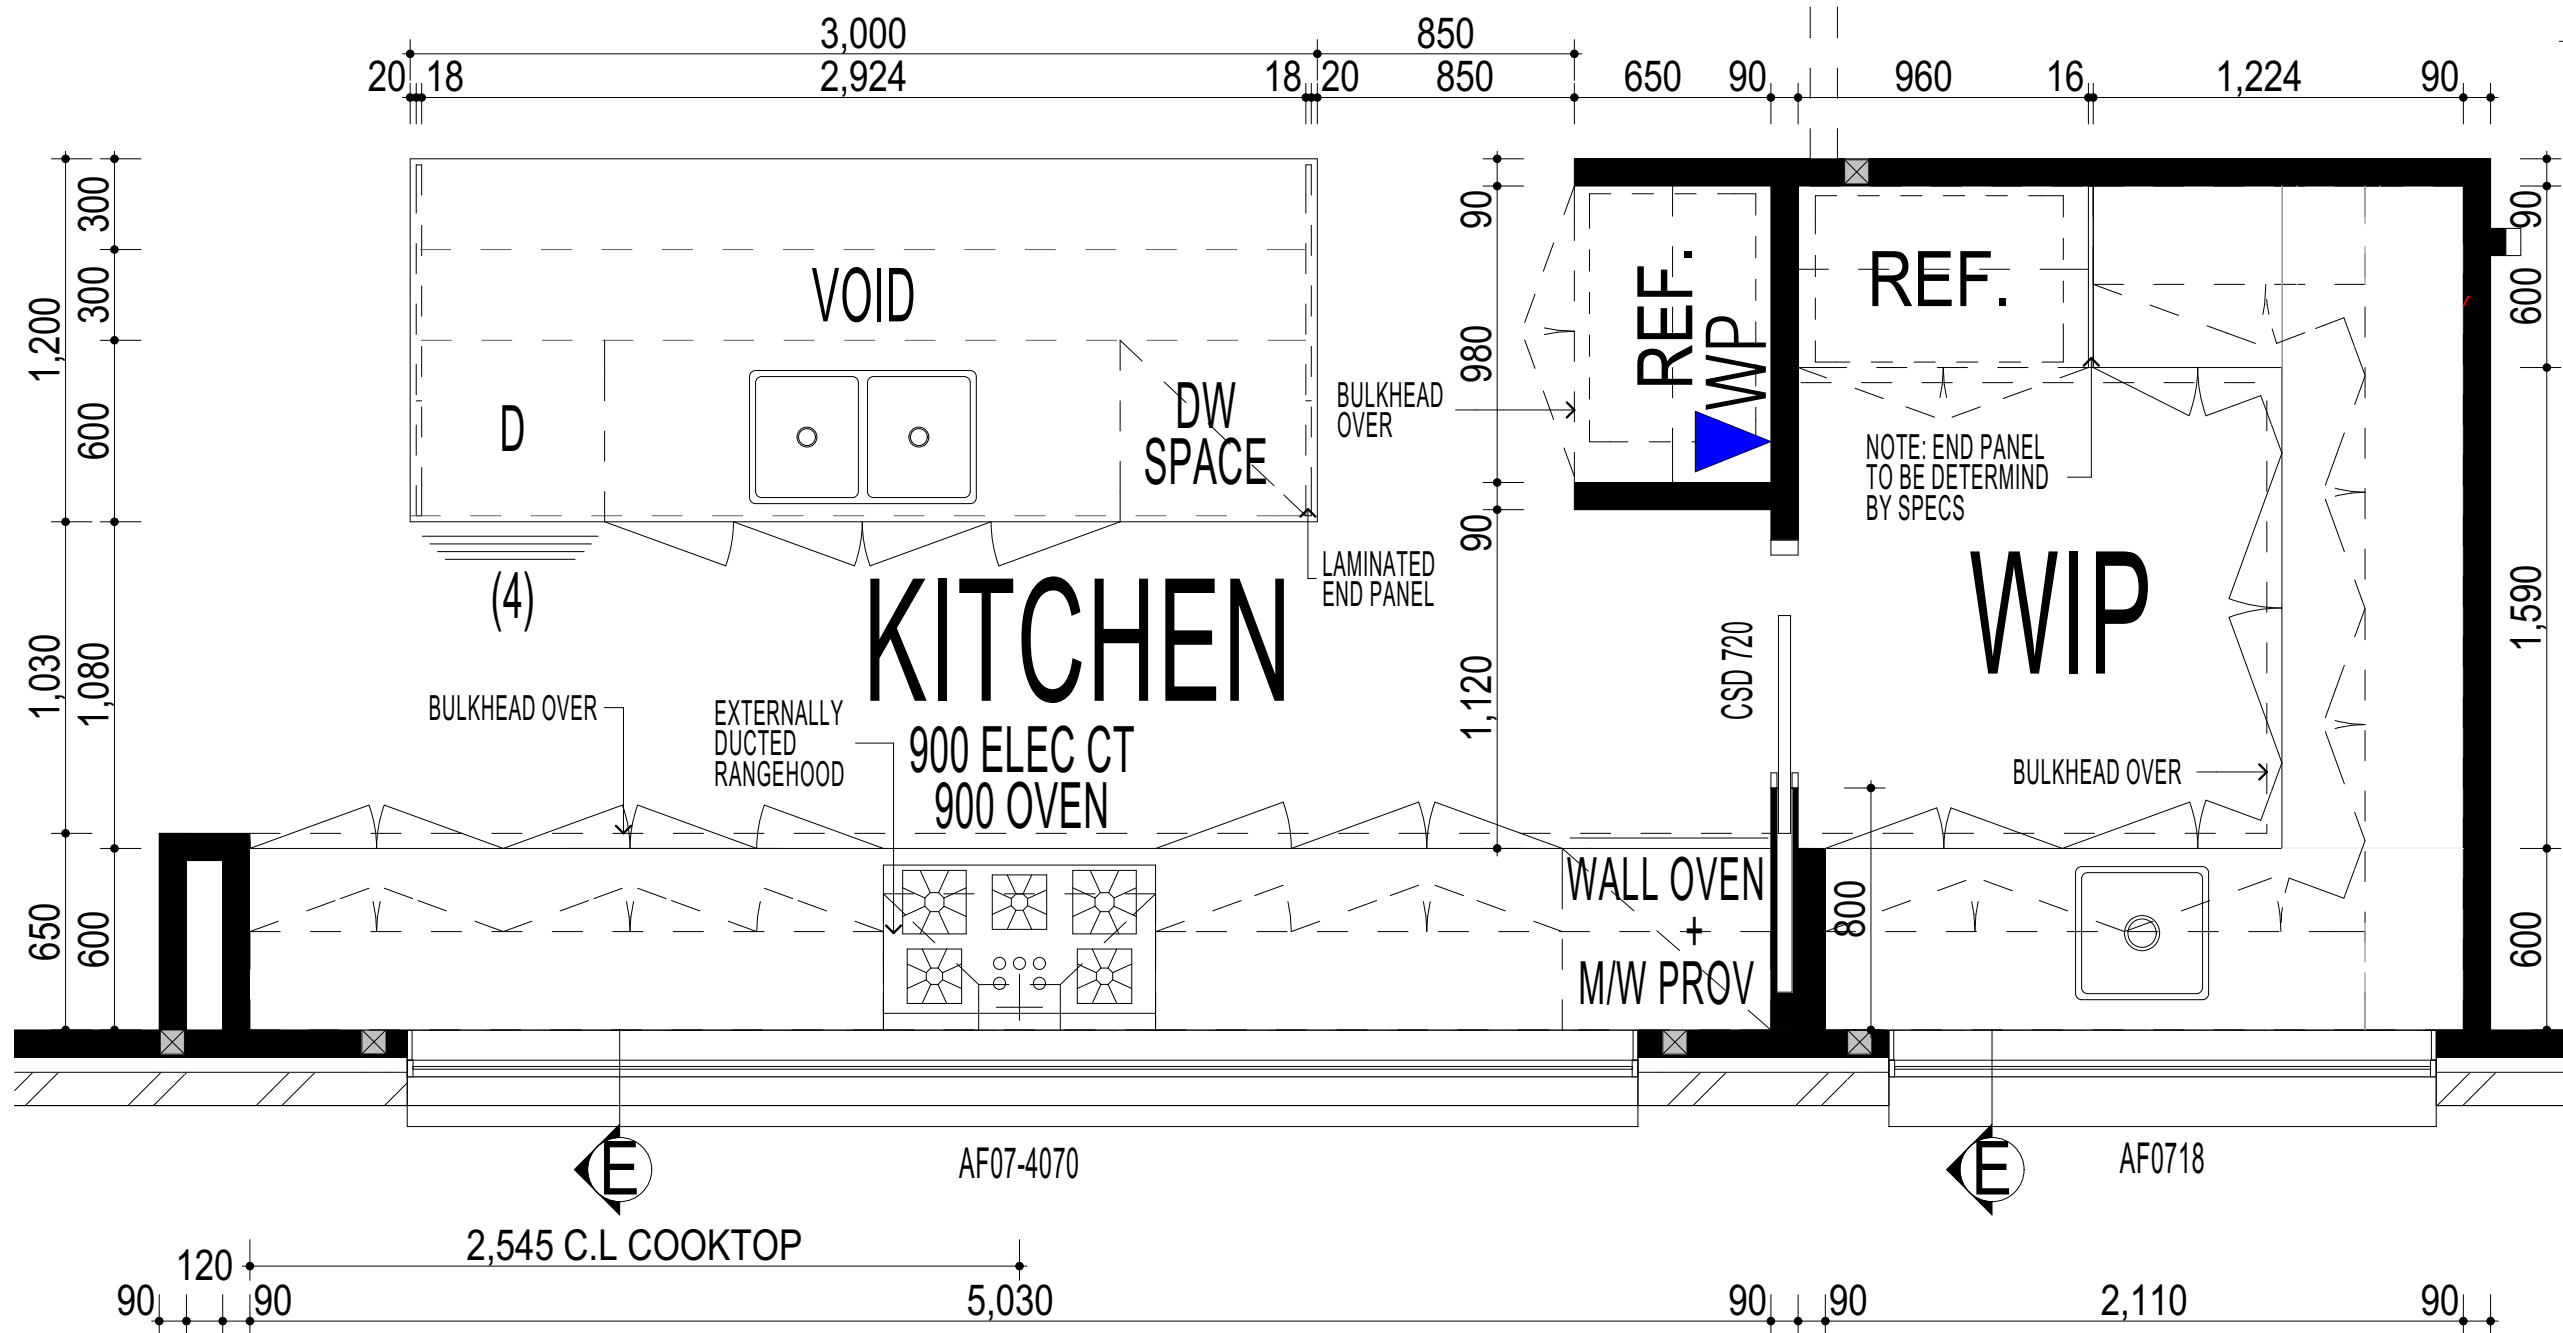

LEGEND:

- 1700mm C/L GPO FOR MICROWAVE PROVISION TO OVERHEAD CUPBOARDS
- 700mm C/L GPO FOR MICROWAVE PROVISION TO BASE CUPBOARDS WITH POT DRAW

PROMOTION:
LUXE PACK

CLIENT:
H. NGUYEN

LOCATION:
**LOT 43B,
101 CAMPBELL STREET,
FAIRFIELD EAST, NSW , 2165**

DP: 358721	council: FAIRFIELD
model: GRANTHAM 36.9 PRISTINE MKII	date: 9/07/2026
Sheet: 11 of 12	checked: P.D.
drawn: J.U./J.L.P	scale: 1:25



5792-25

CLIENT'S SIGNATURE: _____ DATE: _____ S.P.S.M. _____

NOTE:
ALL COMPONENTS SUCH AS: APPLIANCES; PLUMBING FITTINGS & FIXTURES; DOORS; CABINETRY; HANDLES; PC ITEMS; ARE SHOWN ON THE PLANS & ELEVATIONS FOR ILLUSTRATION PURPOSES ONLY & TO COMMUNICATE APPROX SIZES. PLEASE REFER TO YOUR SPECIFICATIONS FOR YOUR RELEVANT INCLUSIONS

KITCHEN DETAILS


- ALL WORK TO BE CARRIED OUT IN ACCORDANCE WITH B.C.A., RELEVANT AUSTRALIAN STANDARDS, LOCAL & STATE ORDINANCES, LOCAL ELECTRICITY, WATER REGULATIONS AND ALL OTHER RELEVANT AUTHORITIES CONCERNED.
- ALL ENGINEERING WORK INCLUDING STRUCTURAL, CIVIL AND SITE DRAINAGE TO BE SUBJECT TO ENGINEER'S DETAILS AND CERTIFICATION AS PER REQUIRED BY COUNCIL.
- ALL WORK TO BE CARRIED OUT IN A PROFESSIONAL AND WORKMANSHIP LIKE WORKMANSHIP LIKE MANNER ACCORDING TO THE PLANS AND SPECIFICATION.
- ALL DIMENSIONS ARE TO BE CHECKED & VERIFIED ON SITE BEFORE COMMENCEMENT OF ANY WORK, ALL LEVELS ARE SUBJECT TO FINAL SURVEY AND SETOUT BY REGISTERED SURVEYOR.
- FIRSTYLE HOMES SITE SAFTEY RULES APPLY.
- DO NOT SCALE FROM DRAWING. LARGER SCALE DRAWINGS & WRITTEN DIMENSIONS TAKE PREFERENCE.
- THIS DRAWING & DESIGN IS COPYRIGHT & THE PROPERTY OF FIRSTYLE HOMES, AND MUST NOT BE RETAINED, COPIED OR USED WITHOUT THE AUTHORITY OF THIS FIRM.

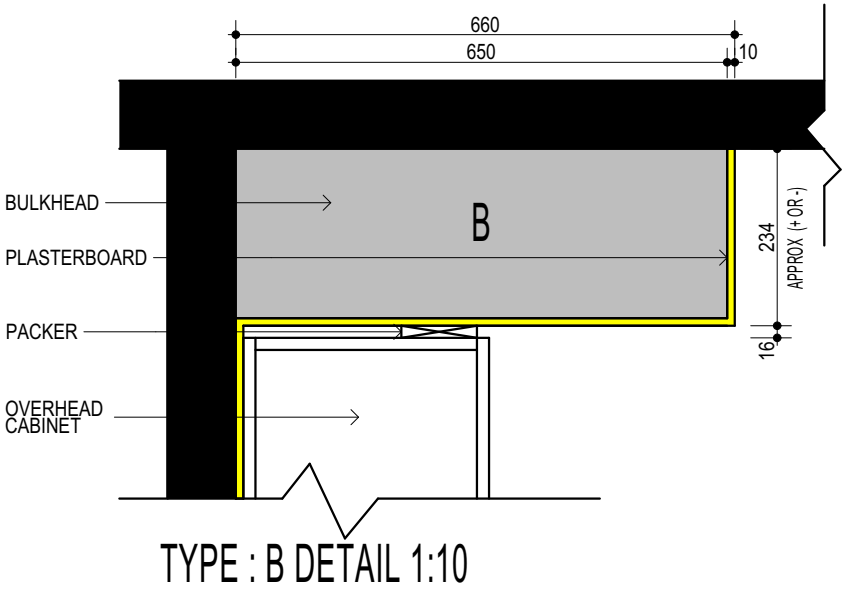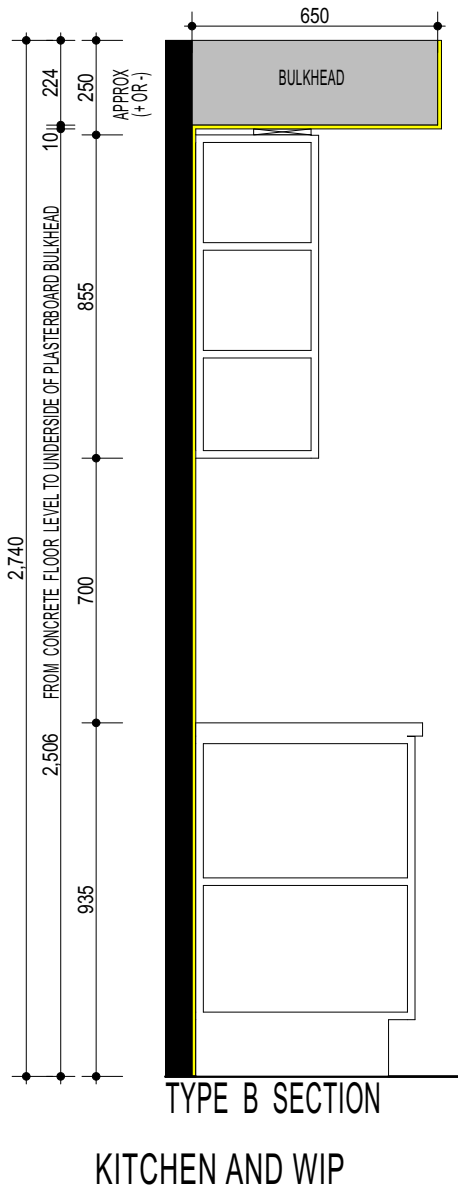


NOTE:
ALL COMPONENTS SUCH AS: APPLIANCES; PLUMBING FITTINGS & FIXTURES; DOORS; CABINETRY; HANDLES; PC ITEMS; ARE SHOWN ON THE PLANS & ELEVATIONS FOR ILLUSTRATION PURPOSES ONLY & TO COMMUNICATE APPROX SIZES. PLEASE REFER TO YOUR SPECIFICATIONS FOR YOUR RELEVANT INCLUSIONS

BULKHEAD DETAILS

PROMOTION:			
LUXE PACK			
CLIENT:			
H. NGUYEN			
LOCATION:			
LOT 43B, 101 CAMPBELL STREET, FAIRFIELD EAST, NSW , 2165			
DP:	council:		
358721	FAIRFIELD		
model:	facade:	date:	quotation assessment:
GRANTHAM 36.9	PRISTINE MKII	9/07/2026	SK1
Sheet:	drawn:	checked:	
12 of 12	J.U./J.L.P.	P.D.	
scale:			
			5792-25
CLIENTS SIGNATURE:		DATE:	
		S.P.S.M...	

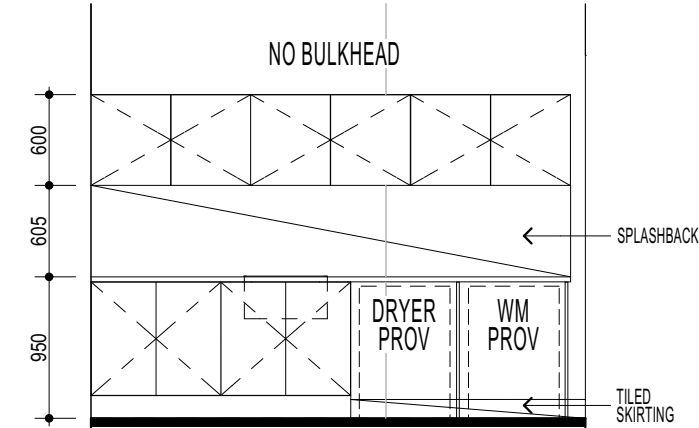


L'DRY ELEVATION
SCALE 1:50

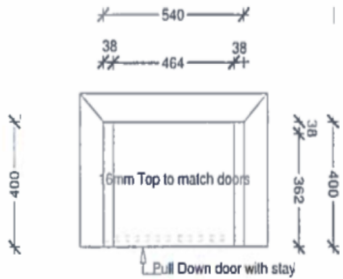

Main Bathroom Chute Cupboard

Please Note: All Dimensions are approximate and will be governed by onsite check measure

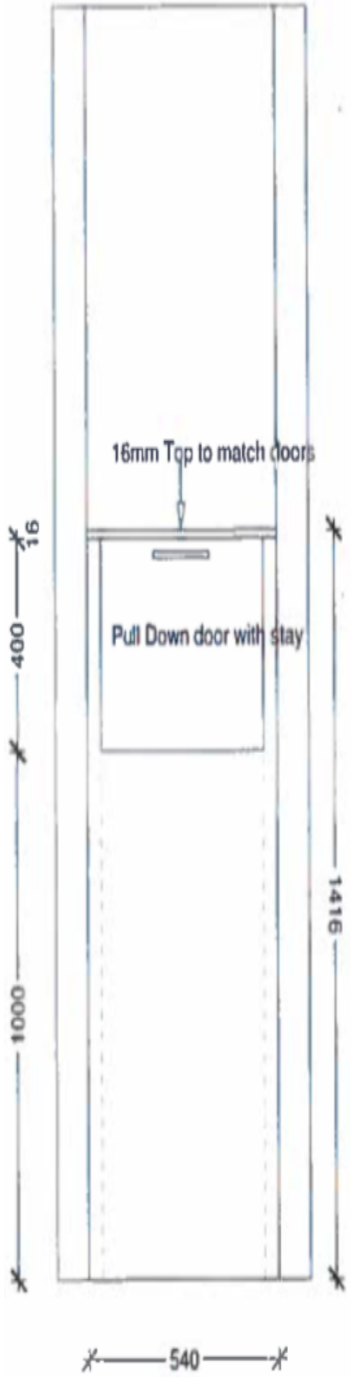

DETAIL R
LAUNDRY CHUTE - NTS



DETAIL R
LAUNDRY CHUTE CABINETRY - NTS

NOTE:
ALL COMPONENTS SUCH AS: APPLIANCES;
PLUMBING FITTINGS & FIXTURES; DOORS;
CABINETRY; HANDLES; PC ITEMS; ARE SHOWN
ON THE PLANS & ELEVATIONS FOR
ILLUSTRATION PURPOSES ONLY & TO
COMMUNICATE APPROX SIZES. PLEASE REFER
TO YOUR SPECIFICATIONS FOR YOUR RELEVANT
INCLUSIONS

LAUNDRY CHUTE DETAILS

PROMOTION: <i>LUXE PACK</i>			
CLIENT: H. NGUYEN			
LOCATION: LOT 43B, 101 CAMPBELL STREET, FAIRFIELD EAST, NSW , 2165			
DP: 358721	council: FAIRFIELD		
model: GRANTHAM 36.9 PRISTINE MKII	facade:	date: 9/07/2026	quotation assessment: SK1
Sheet: 9 of 12	drawn: J.U./J.L.P.	checked: P.D.	scale: 1:50N.T.S
5792-25			
CLIENTS SIGNATURE: _____		DATE: _____ S.P.S.M. _____	